

注册师用章
Registered Engineer

出國專用章

审 定 APPROVE	廖 涛	
审 核 CHECK	伍 俊	
专业负责 SPECIALIST	陈瑞珍	
校 对 CHECK	孙春辉	
校 计 CHECK	陈瑞珍	
制 图 DRAWING		

建设单位 CLIENT	苏州市环境保护局		
工程名称 PROJECT	江苏省环境监测中心及江苏省 环境监察局苏中分局业务用房—主楼		
图名 FILE	一层消防平面图		
设计编号 DRAWING NO.	T08028-ZL		
图例 SYMBOL TABLE	电 池		
日期 DATE	2008.12	图号	24/69



1. 火灾自动报警系统的设备安装应按照《火灾自动报警系统施工及验收规范》施工。
2. 探测器安装位置若与灯具或其他设备的安装间距不能满足规范要求时, 可做适当调整。安装时, 还应保证其距梁边、墙边的距离符合规范要求。
3. 非消防电源切换应在本层配电箱内。

一层消防平面图 1:100


感烟
手报
声光
消火栓
水流、信号
控制模块

地下室, 电梯 12. 200
第 6 页 20


173

电部 174

~~电话 175~~
电梯前室风 176

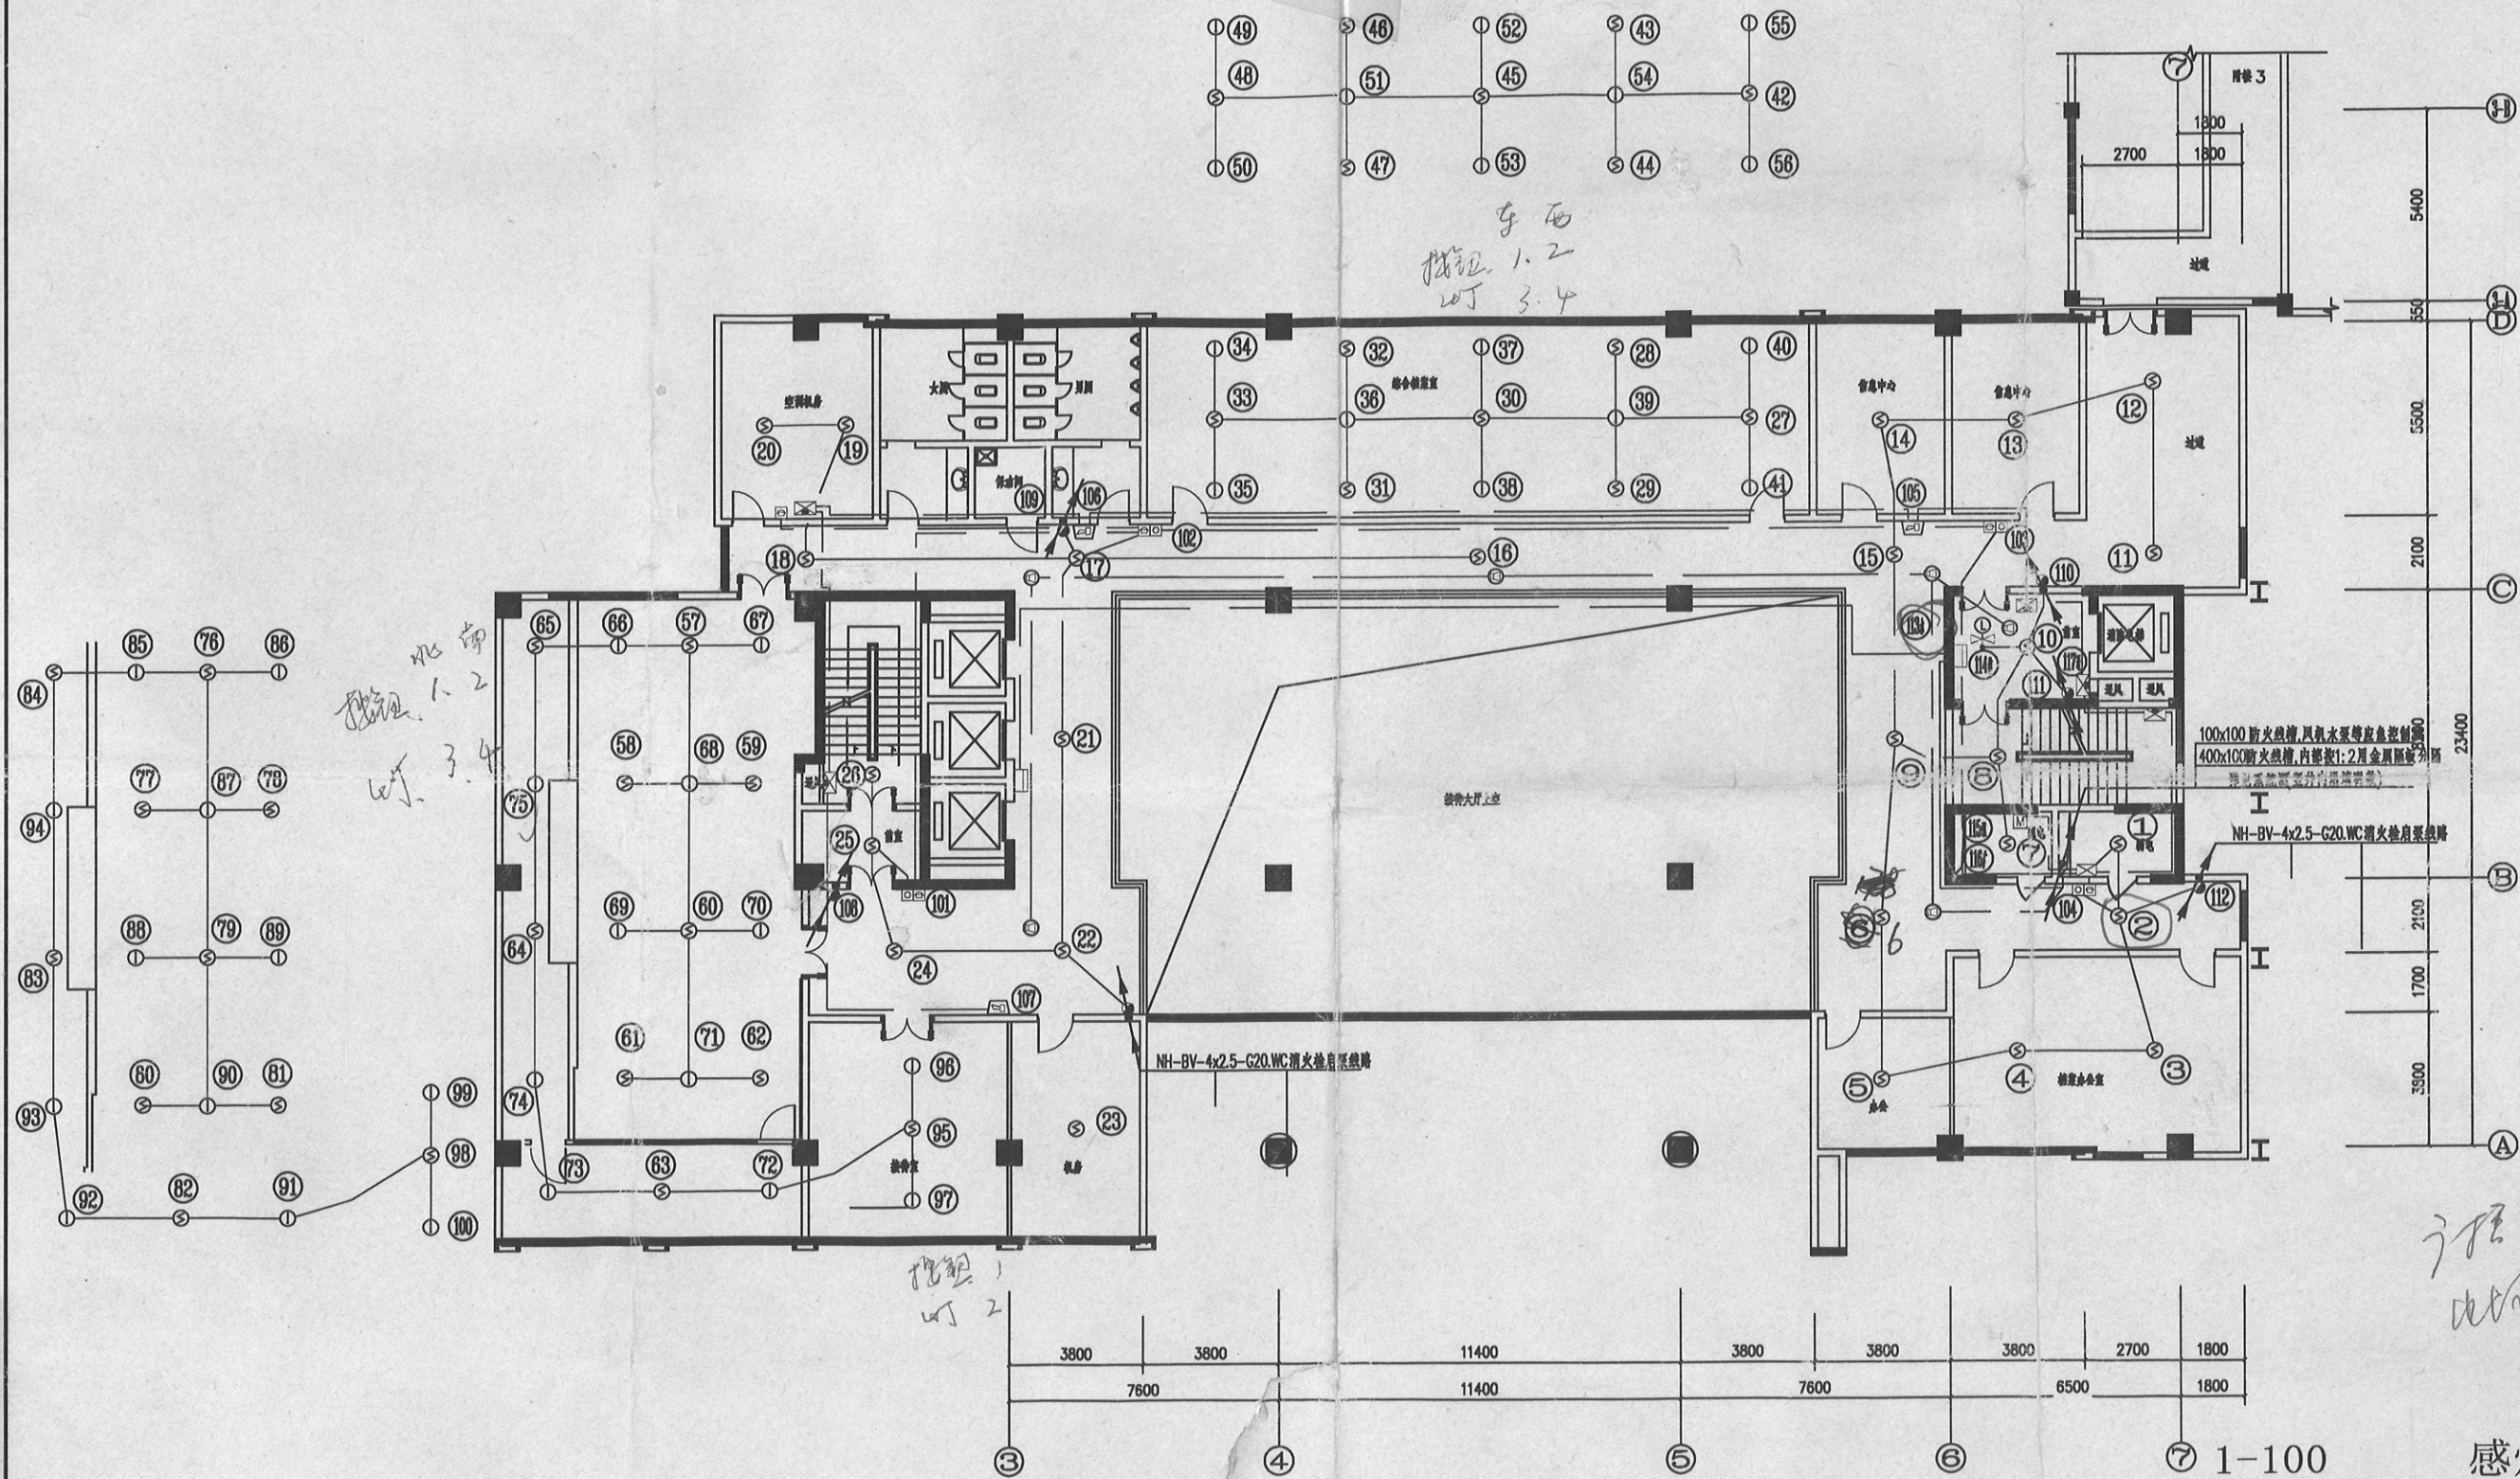

二层消防平面图 1:100

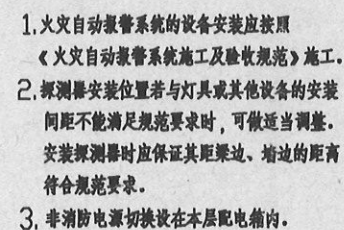

三层消防平面图 1:100

电 194
193

140-177
178-181
182-185
186-190
191-192
193-195

感烟
手报
声光
消火栓
水流、信号
控制模块

合 格			
项目负责 MANAGER	杨洪红	电气 ELECT	
造价 COST		暖通 HVAC	
结构 STRUCT		方案 PLAN	
给排水 PLUMBING			
中水 WATER	陈 浩		
审核 REVIEW	任 俊		
专业负责 SPECIALIST	陈瑞涛		
设计 DESIGN	孙喜厚		
制图 DRAWING	陈瑞涛		

项目编号 CLIENT	泉州市环境保护局		
工程名称 PROJECT	福建省环境监测中心及福建省 环境监察局泉州分局业务用房—主楼		
图名 FILE	三层消防平面图		
设计编号 PROJECT NO.	T08028-ZL		
图例 EXPLANATION	电 池		
日期 DATE	2008.12	图号	26/69



注册师用章

Certified Engineer

出酒會用堂

111

- | 工
業
企
業 | 1 | 2 | 3 | 4 | 5 | 6 | 7 | | | | |
|------------------|---|-------|------|-------|-------|------|------|------|------|------|------|
| 距離 | | 8400 | 2000 | 3800 | 3800 | 3800 | 3800 | 3800 | 3800 | 2700 | 1800 |
| | | 10900 | 5800 | 7600 | 11400 | 7600 | 6500 | 1800 | | | |
| | | | | 49100 | | | | | | | |

四层消防平面图 1:100

感烟
手报
声光
消火栓
水流、信号
控制模块

合 格			
项目负责 PROJECT	杨晓红	电气 ELECT	
质量 QUALITY		暖通 HEATING	
结构 STRUCTURE		油漆 PAINTING	
给排水 PLUMBING			
专业 SPECIALIST	廖 洁		
审核 REVIEWER	任 俊		
专业负责 SPECIALIST	陈瑞洁		
校对 CHECKER	潘春辉		
设计 DESIGNER	陈瑞洁		
制图 DRAWING			
批准/审核 CLIENT	泰州市环境保护局		
工程名称 PROJECT	江苏省中环境安全中心及江苏省 环境监察局中分局业务用房—主楼		
图 名 TITLE	四层消防平面		
收图日期 RECEIVED DATE	T08026—ZL		
图 册 DRAWING BOOK	2008.12	册数 NUMBER	27/06


用途
消防

注册师用章
注册工程师

出图用章
出图章

专业	
建筑	电气
结构	暖通
给排水	动力
弱电	照明
空调	消防
人防	其他

建设单位	泰州市环境保护局
工程名称	江苏省泰州经济开发区污水处理厂
设计单位	无锡市建筑设计研究院
项目名称	五层消防平面图
设计编号	T08028-ZL
日期	2008.12
图号	28/69

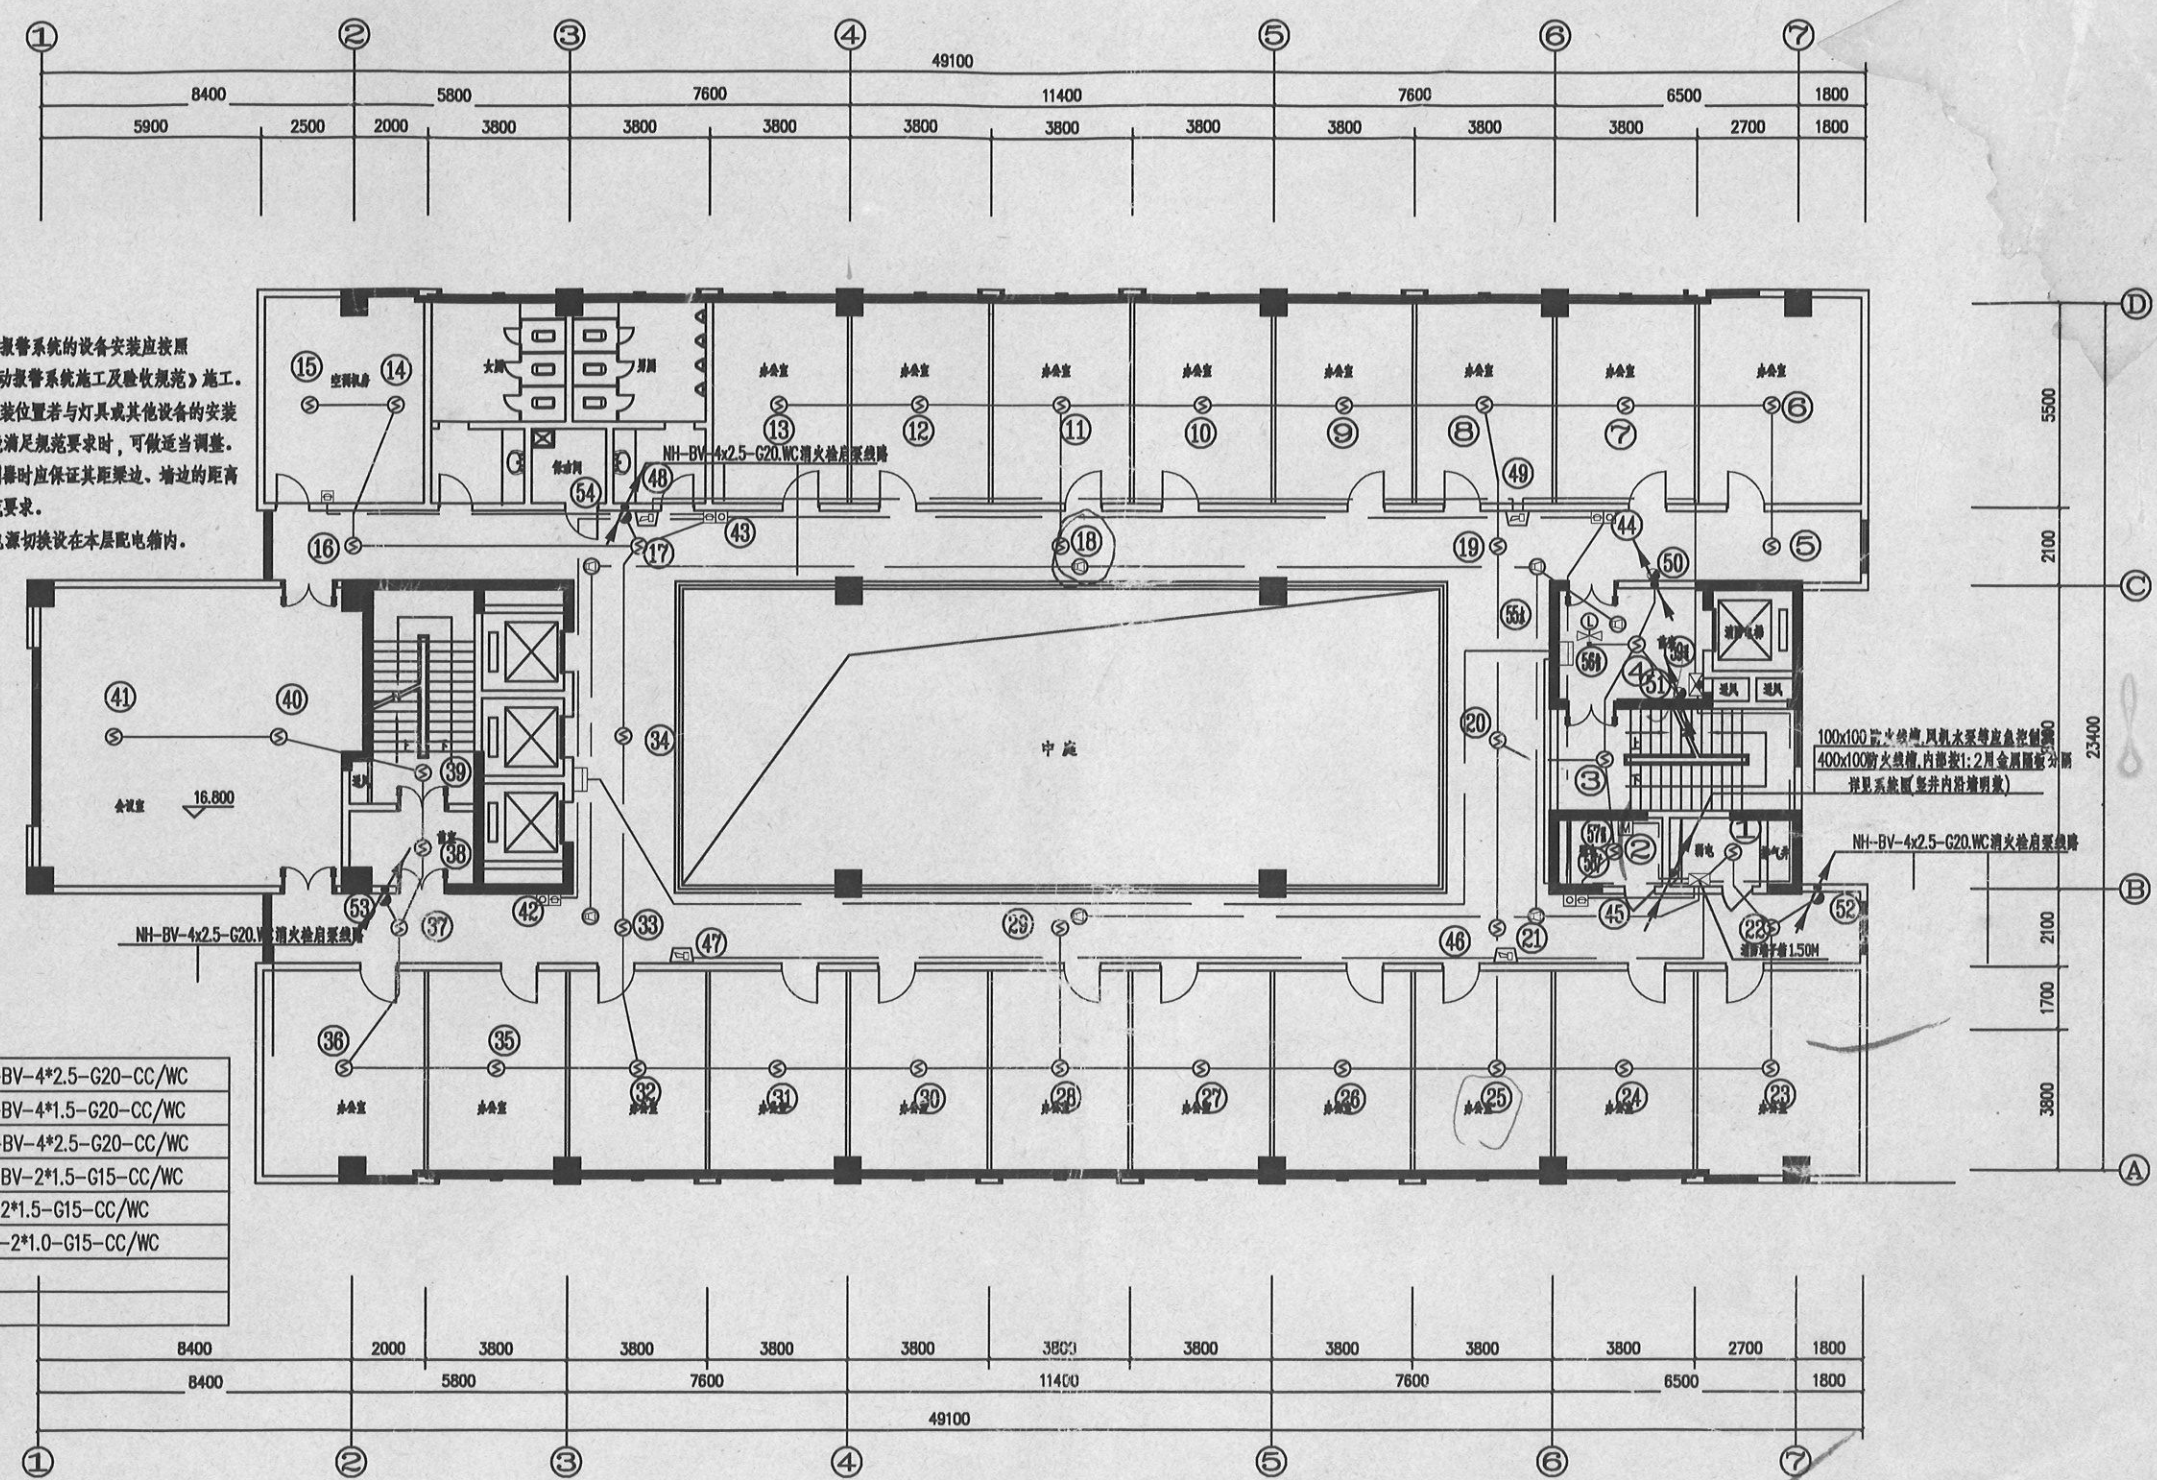

1. 火灾自动报警系统的设备安装应按照《火灾自动报警系统施工及验收规范》施工。
2. 探测器安装位置若与灯具或其他设备的安装间距不能满足规范要求时, 可做适当调整。安装探测器时应保证其距梁边、墙边的距离符合规范要求。
3. 非消防电源切换设在本层配电箱内。

— FK —	消防联动总线	NH-BV-4*2.5-G20-CC/WC
— FX —	显示总线	NH-BV-4*1.5-G20-CC/WC
— FK1 —	消火栓启泵控制线	NH-BV-4*2.5-G20-CC/WC
— FH —	消防电话线	NH-BV-2*1.5-G15-CC/WC
— — —	消防报警总线	BV-2*1.5-G15-CC/WC
— G —	消防广播线	RVS-2*1.0-G15-CC/WC

五层消防平面图 1:100

57. 消防
58. 电话
59. 对讲
- | | |
|-------|-------|
| 1-41 | 感烟 |
| 42-45 | 手报 |
| 46-49 | 声光 |
| 50-54 | 消火栓 |
| 55-56 | 水流、信号 |
| 57-59 | 控制模块 |

注册师用章

出国专用章

建设单位 CLIENT	泰州市环境保护局		
工程名称 PROJECT	江苏省生态环境信息中心江苏省 生态环境监测中心业务用房—主楼		
图名 FILE	大厦消防平面图		
设计编号 PROJECT NO.	T08028-ZL		
图号 FILE NO.	电施		
日期 DATE	2008.12	图号 FILE NO.	29/69



196. 订售
197. 电切
198. 东北锦
199. 西村锦

140-180
181-184
185-188
189-193
194-195
196-200

感烟
手报
声光
消火栓
水流、信号
控制模块

Z_1, Z_2 无电压
 D_1, D_2 27V

注册师用章
Certified Engineer

出图专用章


[illegible]

九层消防平面图 1:100

注册师用章

出图专用章

合 格 COMPLY			
项目负责 PROJECT LEADER	梅红松	电气 ELECTRICIAN	
商务 BUSINESS		暖通 HEATING	
给排水 PLUMBING		方案 DESIGN	
结构 STRUCTURE			
审查 CHECK	邵 涛		
审查 CHECK	任 俊		
专业负责 SPECIALIST	陈瑞峰		
校核 CHECK	潘春海		
设计 DESIGN	陈瑞峰		
审核 CHECK			
批准 APPROVE			
批准单位 CLIENT	泰州市环境保护局		
工程名称 PROJECT	江苏省中环境设计中心及江苏省 环境监察局会议中心业务用房—主楼		
图 名 TITLE	十层楼梯平面图		
设计编号 DESIGN NO.	T08028—ZL		
日期 DATE	电气	签字 SIGNATURE	33/61
日期 DATE	2008.12		

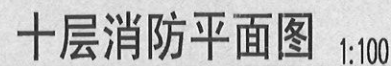

70-110	感烟
111-114	手报
115-118	声光
119-123	消火栓
124-125	水流、信号
126-128	控制模块

附注

NOTES

注册师用章

Registered Engineer


出图专用章

Issue Seal

工程概况			
项目名称	名称	地址	性质
建设单位	名称	地址	性质
设计单位	名称	地址	性质
监理单位	名称	地址	性质

专业	姓名	职称
建筑	姓名	职称
结构	姓名	职称
给排水	姓名	职称
暖通	姓名	职称
电气	姓名	职称
暖通	姓名	职称

批准	无锡市环境保护局
审核	无锡市环境保护局
设计	无锡市环境保护局
制图	无锡市环境保护局
校对	无锡市环境保护局
审核	无锡市环境保护局
批准	无锡市环境保护局
设计	无锡市环境保护局
制图	无锡市环境保护局
校对	无锡市环境保护局
审核	无锡市环境保护局
批准	无锡市环境保护局

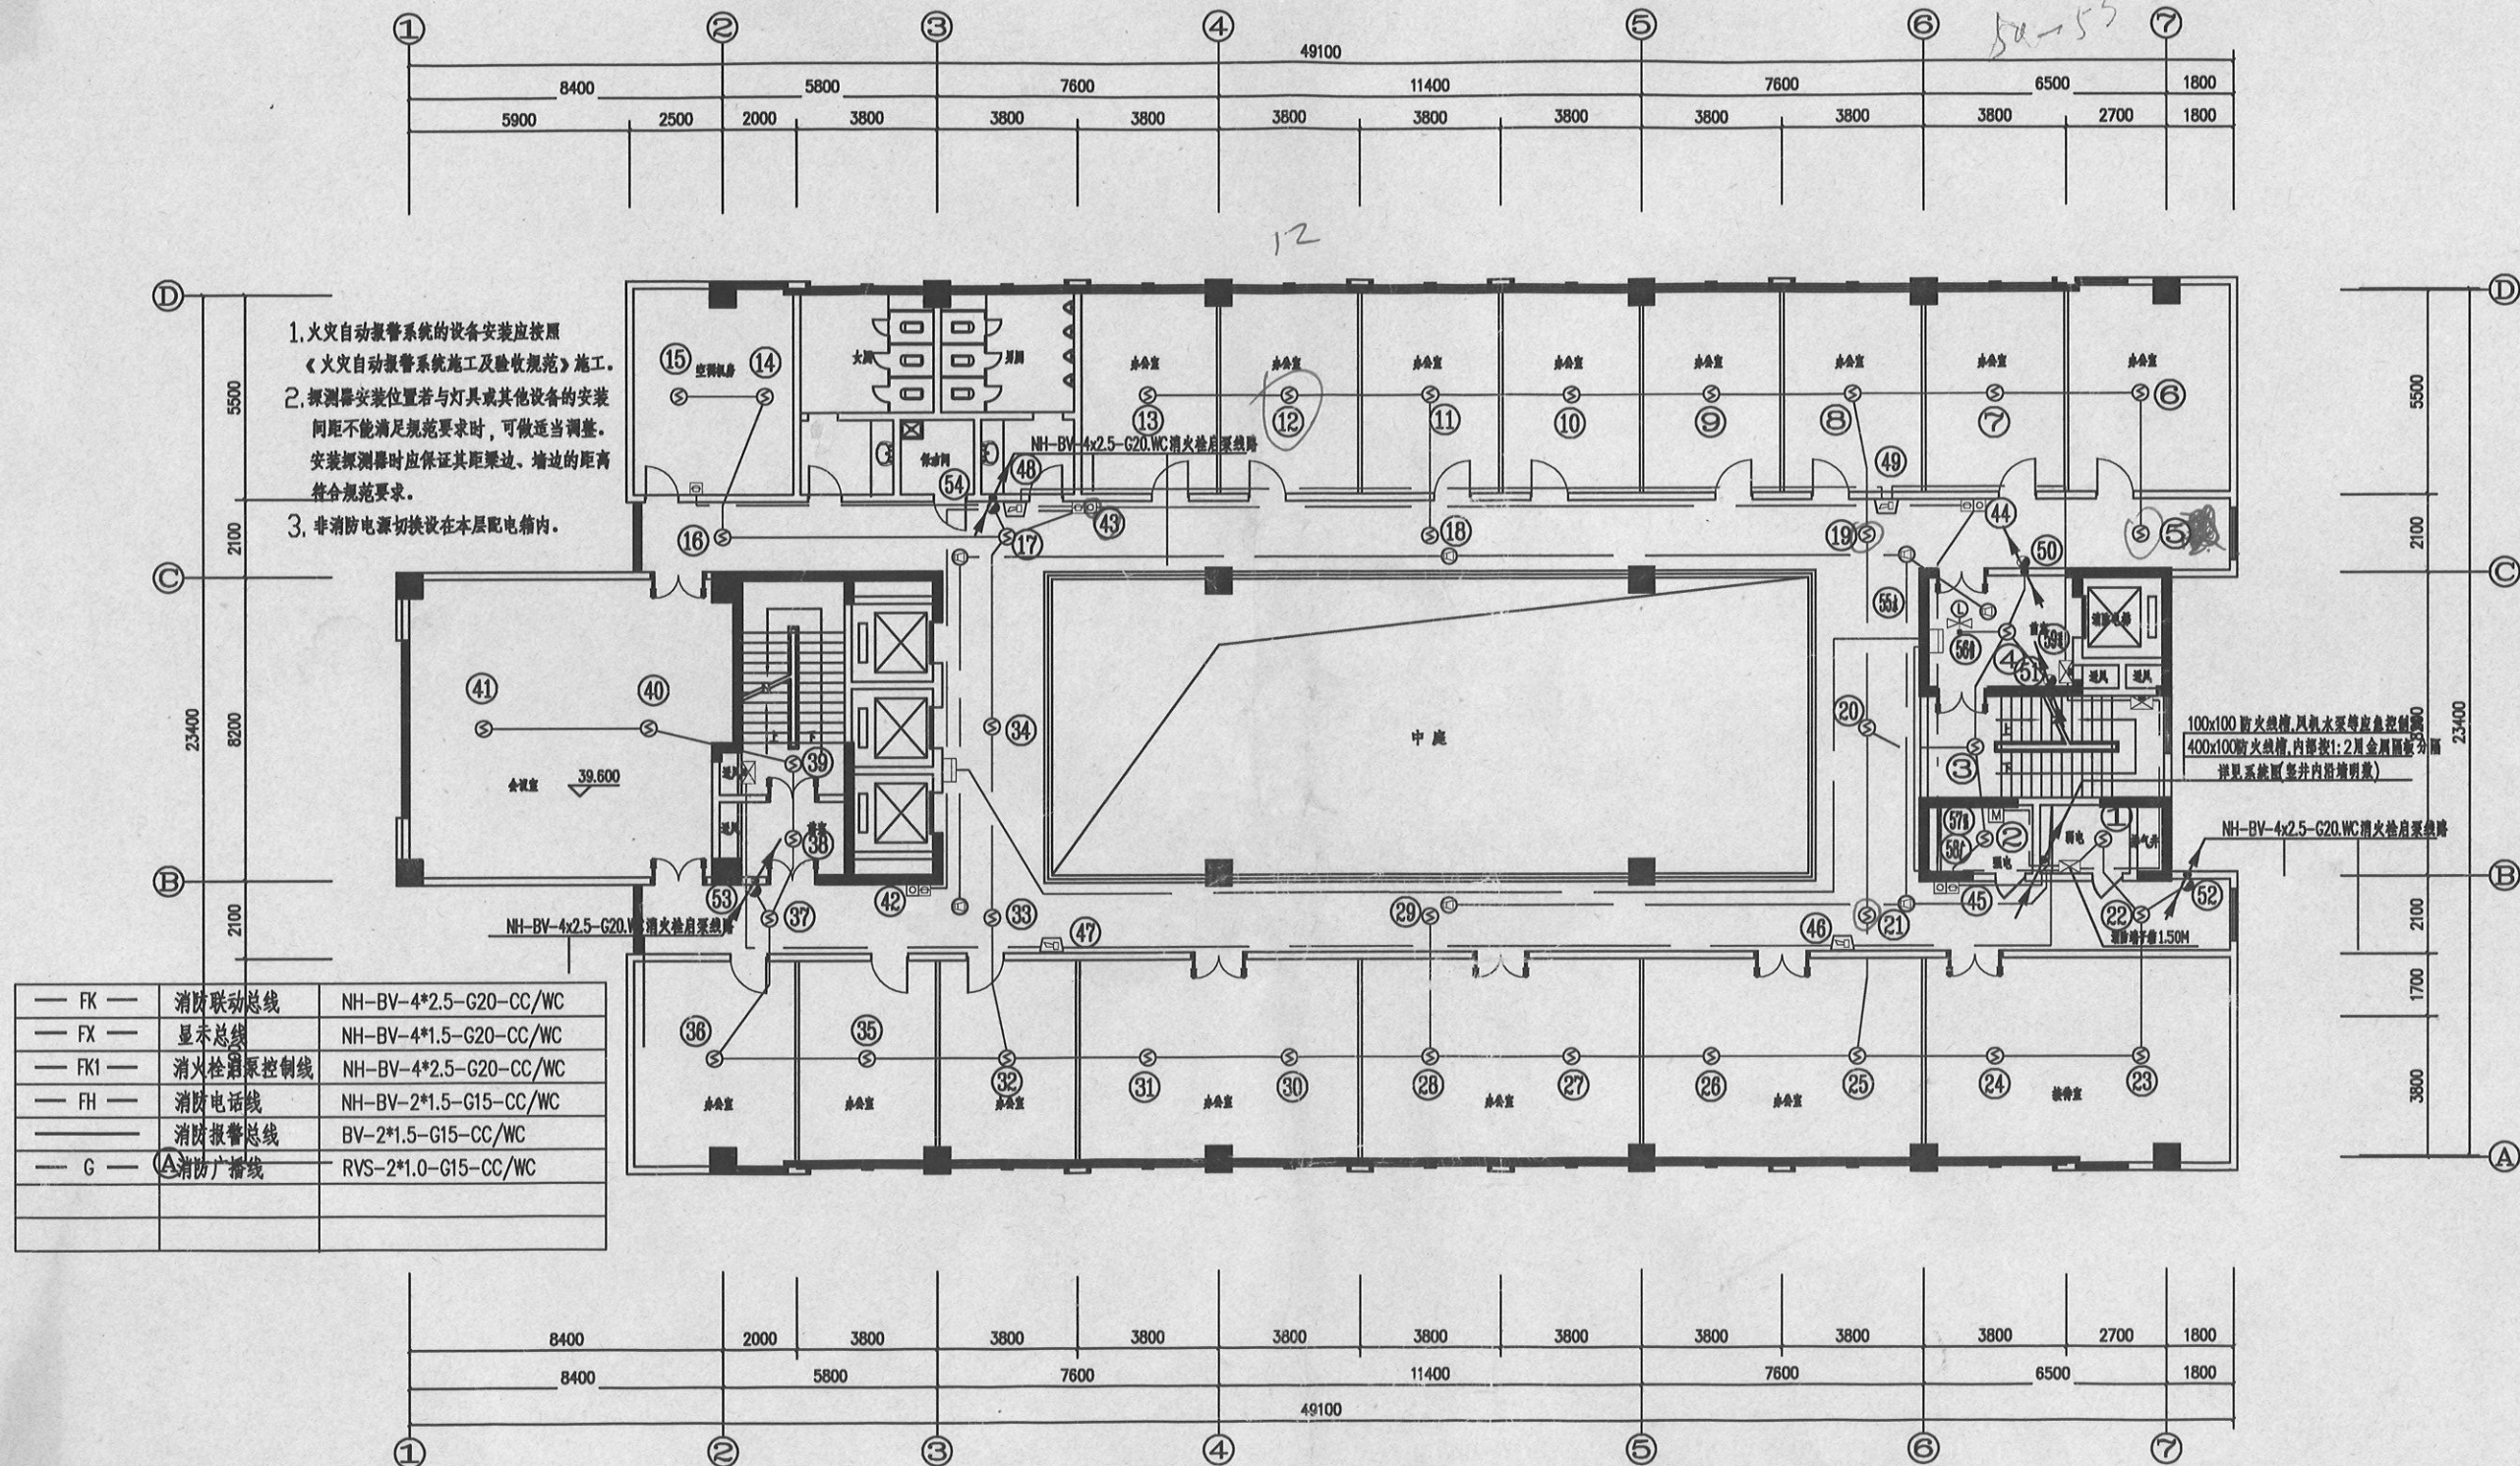

十一层消防平面图 1:100

- 1-41 感烟
42-45 手报
46-49 声光
50-54 消火栓
55-56 水流、信号
57-59 控制模块

注册师用章
Certified Bookkeeper

出图专用章	
-------	--

[illegible]

十二层消防平面图 1:100

注册师用章

出国专用章

委托人 CLIENT	泰州市环境保护局		
工程名称 PROJECT	江苏省集中饮用水源地水质及江苏省 环境监察局泰州分局业务用房—主楼		
图名 TITLE	十三层消防平面图		
设计编号 PROJECT NO.	T08028-ZL		
图例 SYMBOLS	电梯		
日期 DATE	2008.12	图号	36/69




附注

注册师用章

出图专用章

工程概况			
工程名称	无锡市环境检测中心	建设单位	无锡市环境检测中心
工程地址	无锡市环境检测中心	设计单位	无锡市建筑设计研究院
工程规模	无锡市环境检测中心	监理单位	无锡市环境检测中心
工程性质	无锡市环境检测中心	施工单位	无锡市环境检测中心
工程日期	无锡市环境检测中心	竣工日期	无锡市环境检测中心
工程阶段	无锡市环境检测中心	设计阶段	无锡市环境检测中心
工程内容	无锡市环境检测中心	设计内容	无锡市环境检测中心
工程负责人	无锡市环境检测中心	设计负责人	无锡市环境检测中心
工程审核人	无锡市环境检测中心	设计审核人	无锡市环境检测中心
工程审批人	无锡市环境检测中心	设计审批人	无锡市环境检测中心
工程验收人	无锡市环境检测中心	设计验收人	无锡市环境检测中心
工程竣工人	无锡市环境检测中心	设计竣工人	无锡市环境检测中心
工程交付人	无锡市环境检测中心	设计交付人	无锡市环境检测中心
工程移交人	无锡市环境检测中心	设计移交人	无锡市环境检测中心
工程归档人	无锡市环境检测中心	设计归档人	无锡市环境检测中心
工程销毁人	无锡市环境检测中心	设计销毁人	无锡市环境检测中心

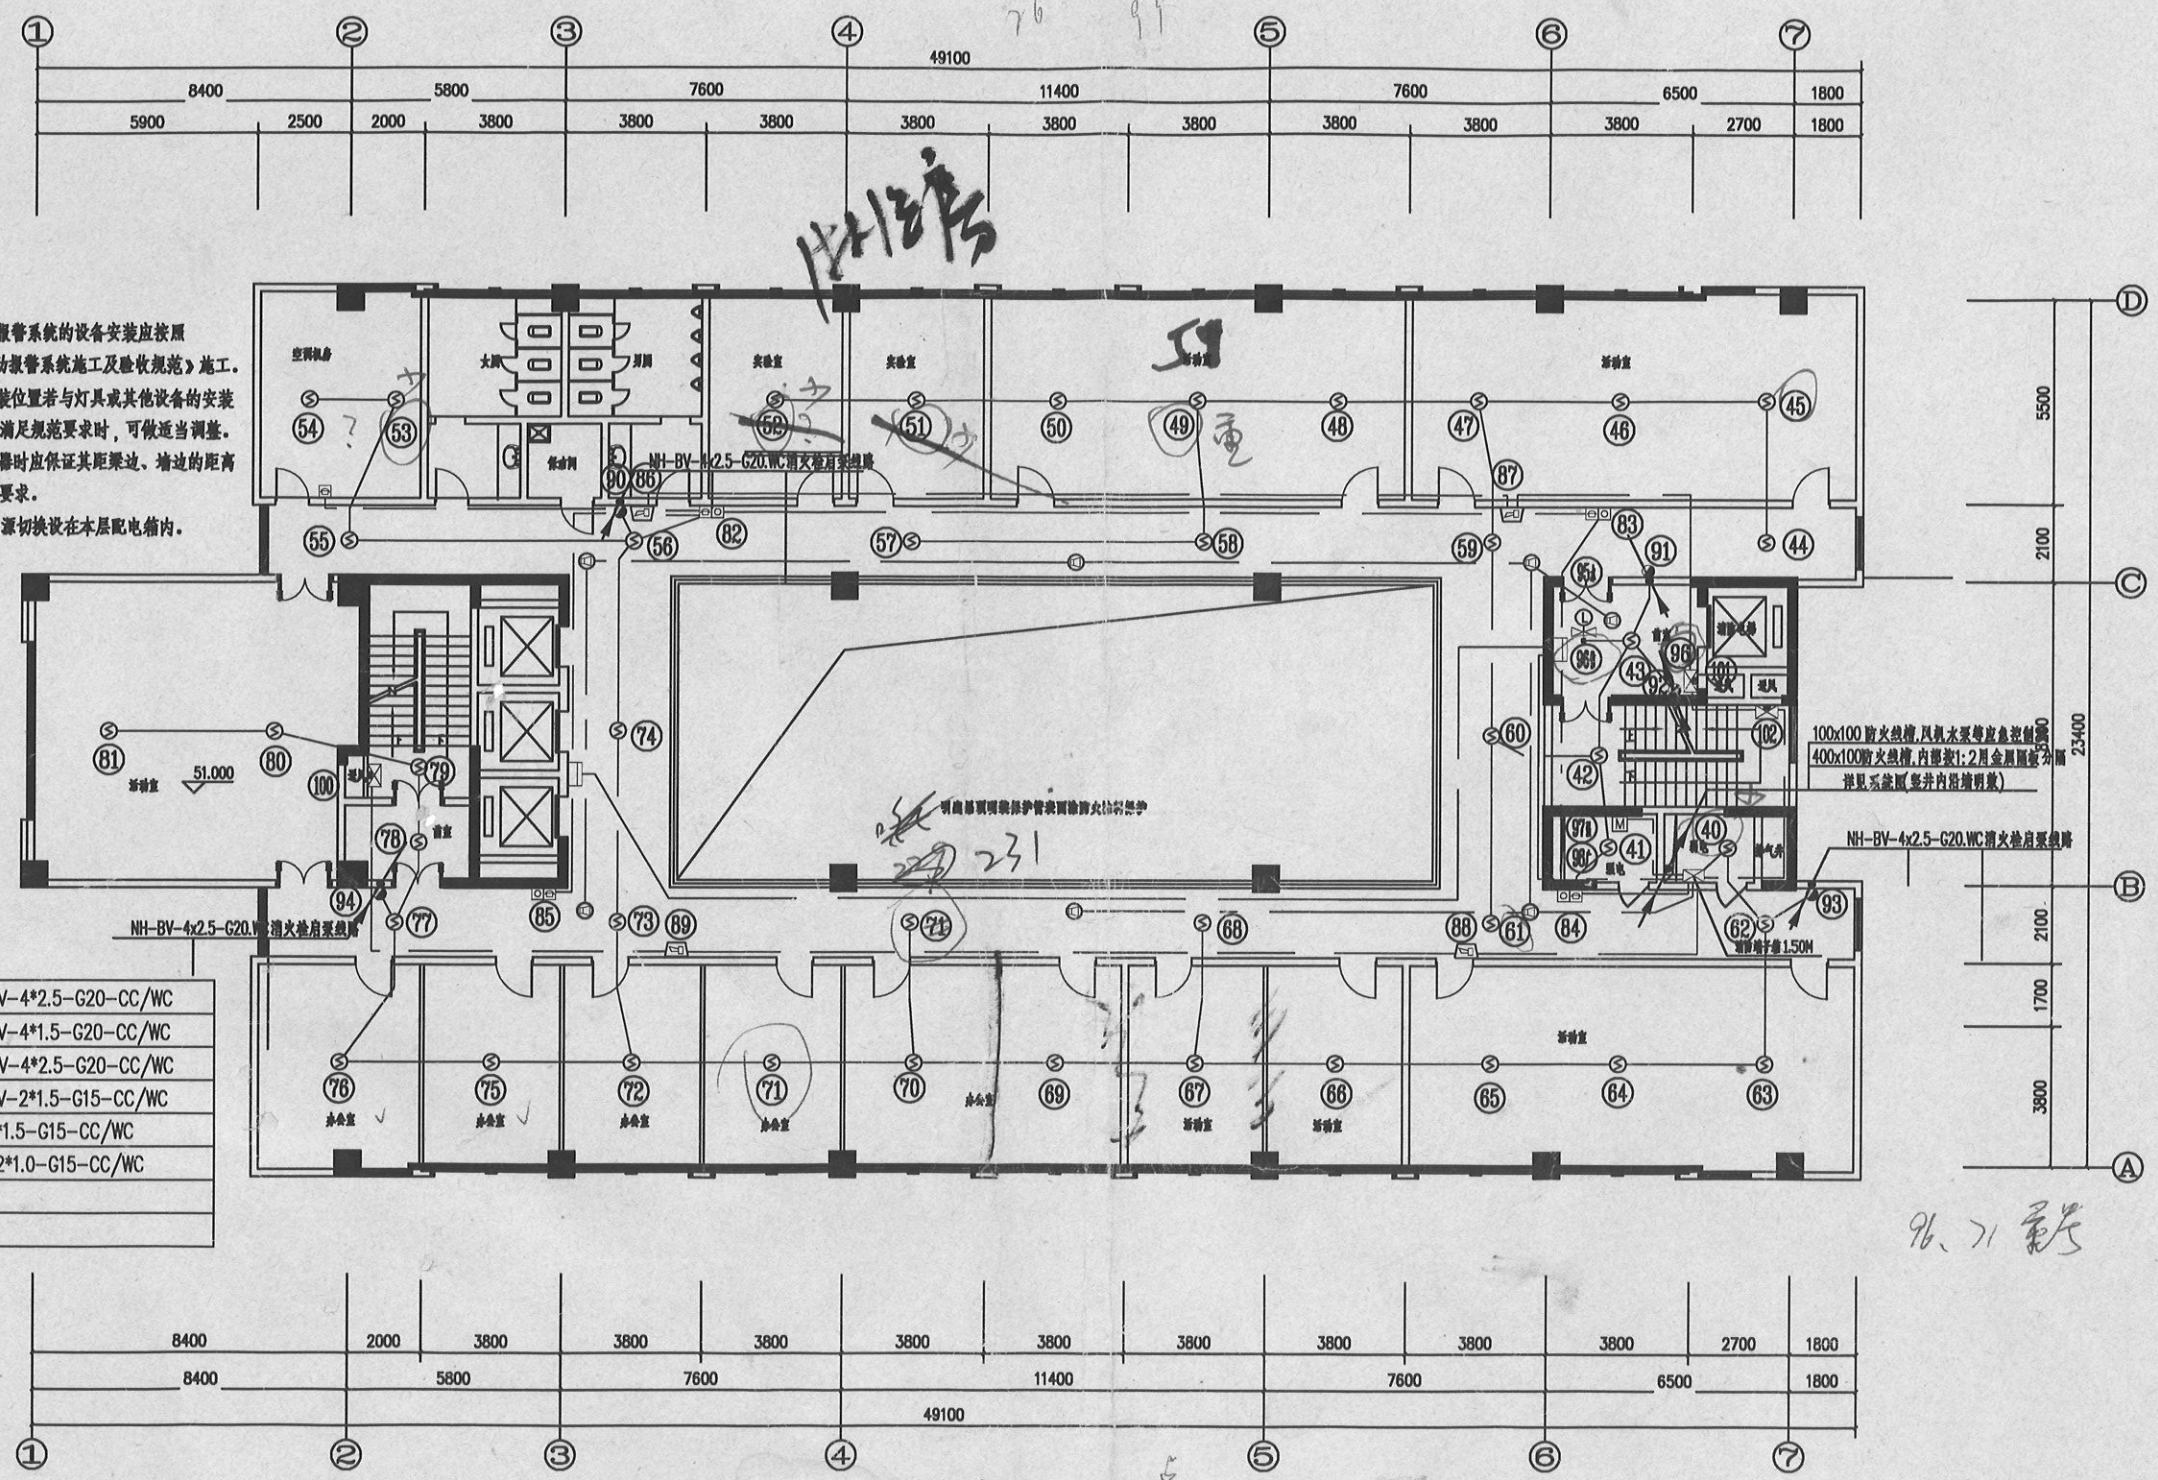

十四层消防平面图 1:100

— FK —	消防联动总线	NH-BV-4*2.5-G20-CC/WC
— FX —	显示总线	NH-BV-4*1.5-G20-CC/WC
— FK1 —	消火栓启泵控制线	NH-BV-4*2.5-G20-CC/WC
— FH —	消防电话线	NH-BV-2*1.5-G15-CC/WC
— — —	消防报警总线	BV-2*1.5-G15-CC/WC
— G —	消防广播线	RVS-2*1.0-G15-CC/WC

- 40-80 感烟 81. 229 230
- 81-85 手报
- 86-89 声光
- 90-94 消火栓 91. 92 未编
- 95-98 水流 99 信号
- 97-102 控制模块