
 申都设计集团 SHENDU DESIGN GROUP		图纸目录							
		项目名称 Project Name		项目编号 Project No.					
		子项名称 Sub-Project		子项编号 Sub-Project No.					
		图纸名称 Sheet Title		阶 段 Stage		施工图			
		专 业 Discipline		电 气		版 次 Rev.		1	
建设单位 Client		扬子江药业集团有限公司		图 号 Sheet No.		日 期 Date		2024.8.15	
序号	图号	图纸名称			图幅	版次	备注		
1	电施-01	设计说明 火灾自动报警及联动系统图			A1	1			
2	电施-02	一层火灾自动报警平面图			A1+	1			
3	电施-03	二层火灾自动报警平面图			A1+	1			
4	电施-04	三层火灾自动报警平面图			A1+	1			
5	电施-05	四层火灾自动报警平面图			A1+	1			
6	电施-06	一层照明平面图			A1+	1			
本图须加盖出图签章, 否则一律无效 Invalid Unless Stamped									
职 责 Responsibility	审 定 Approved by	设计负责人 Principal in charge	审 核 Reviewed by	校 对 Checked by	专业负责人 Discipline Responsible	设 计 Designed by	绘 图 Drawn by		
姓 名 Name									
签 字 Signature									

会 答	建 筑	给 排 水	强 电	影 响	动 力
Confirmed by	Architectures	Trunk Sewerage	Electricity	Landmark	Power
	结 构	通 风	弱 电	室 内	人 防
	Structures	Vent	Equip	Interiors	[Civil air defense]

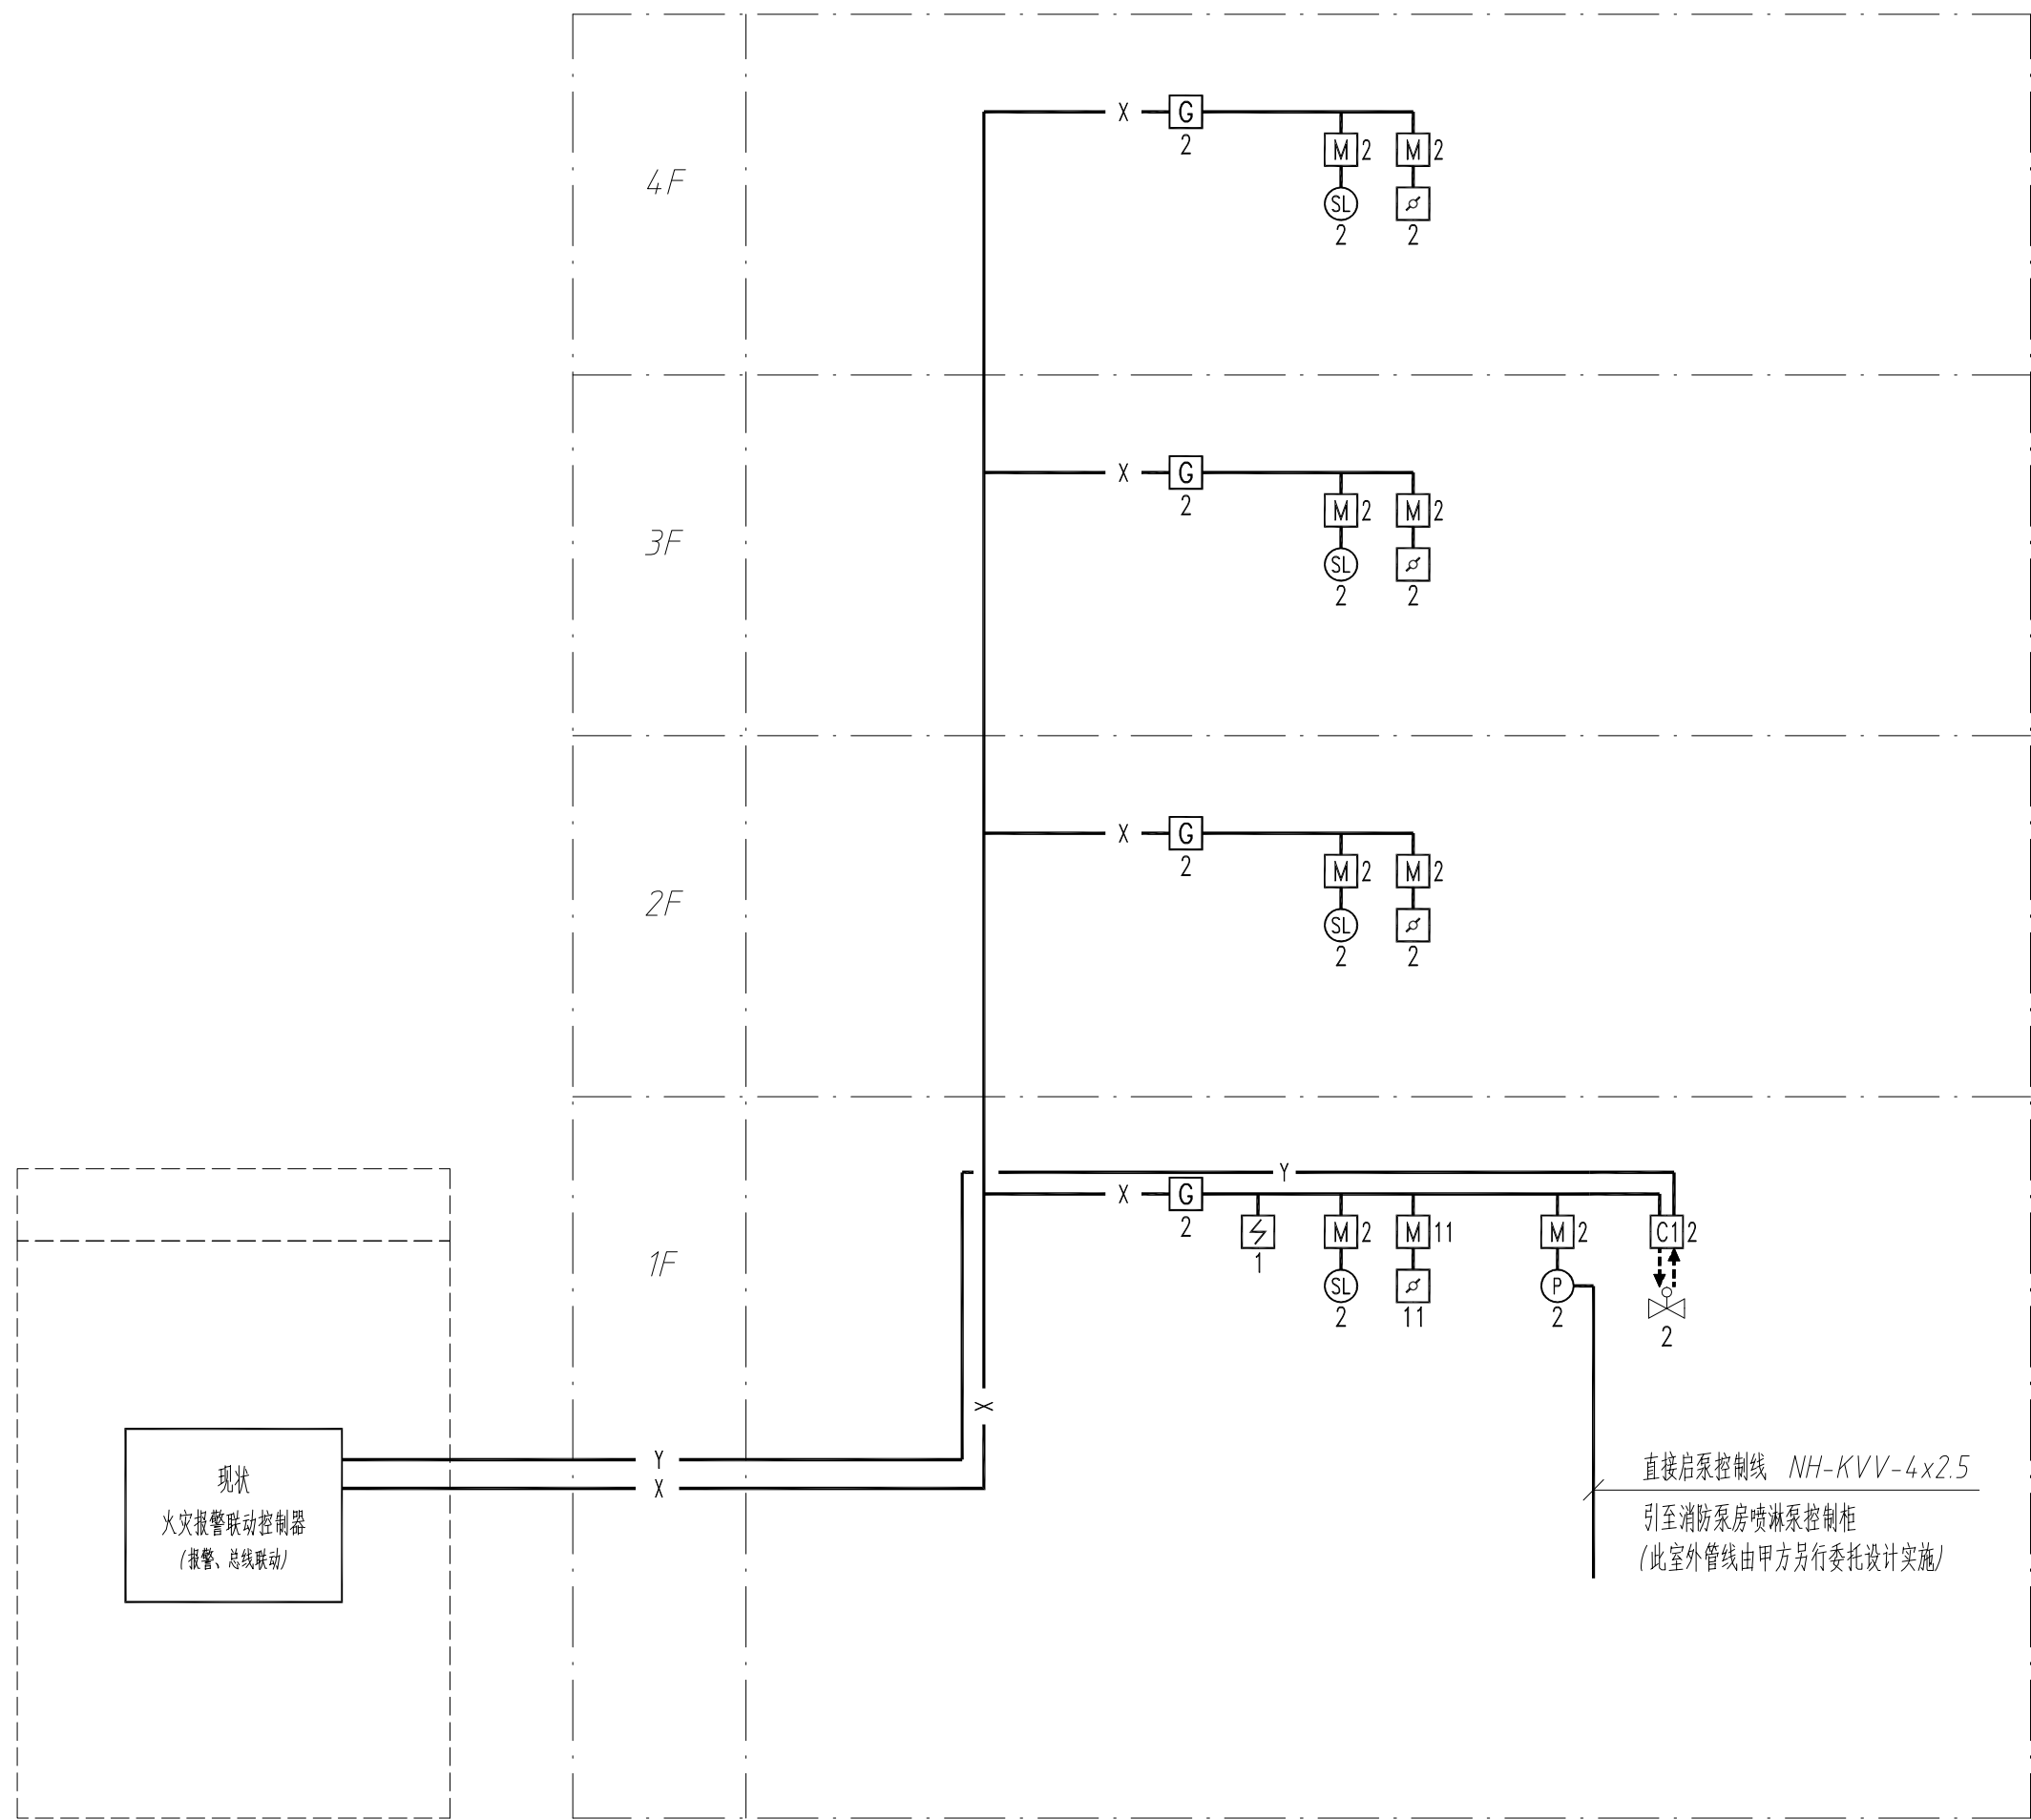

火灾自动报警及联动系统图

序号	名 称	型号及规格	图例	单位	备 注
1	点型光电感烟火灾探测器	同现状产品		只	项质
2	输入模块	同现状产品		只	项质/设备附近安装
3	单输入输出控制模块	同现状产品		只	
4	总线按钮报警器	同现状产品		只	项质或壁装 (距地 1.5m)
5	信号阀	见给排水专业图纸		只	
6	水流指示器	见给排水专业图纸		只	
7	压力开关	见给排水专业图纸		只	
8	电磁阀	(DC24V) 见给排水专业图纸		只	

设计说明:

1、工程概况:

本工程为扬子江药业集团清公司—综合仓库改造工程项目，项目位于泰州市扬子江药业集团有限公司厂区内。原建筑总建筑面积 10367.6m^2 ，本次改造面积： 10367.6m^2 ，主要功能为药材原料仓库。本工程是在现有消防设施基础条件下，加强消防设施—即新增自动喷水（预作用）灭火系统（不充气单联锁），提高该仓库的消防安全性。建筑类型：多层丙类建筑，本次改造不改动该建筑类型。

2、根据《江苏省既有建筑改造消防技术标准》（试行）《2023年7月版》，本项目属于“建筑内部装修”，电气专业的相关消防系统适用原标准；复核本项目原设计图纸出图时间为2014年02月。

3、电气专业设计内容如下:

3.1 每层按防火分区增加信号阀、水流指示器报警;

3.2 一层新增报警阀间内信号阀、压力开关、电磁阀报警及联动控制;

3.3 一层新增报警阀间照明设计。

4、自动喷水灭火系统联动控制:

4.1 系统干管压力开关、湿式报警阀压力开关、高位水箱出水管的流量开关的动作信号作为触发信号,直接控制启动喷淋泵,联动控制不应受消防联动控制器处于自动或手动状态影响。

4.2 预作用装置控制方式:当火灾报警系统接收到联动触发信号(即火灾确认信号),应采用二个独立的报警触发装置报警信号的“与”逻辑组合/后,联动控制器发出联动控制信号,启动相应楼层的预作用装置的电磁阀,从而启动预作用装置。

4.3 上述设备的动作信号传输至消防报警主机,消防控制室可通过控制模块编程,自动启动喷淋泵,并接收其反馈信号。

4.4 喷淋泵控制柜的启动、停止按钮用专用线路直接连接至消控室的手动控制盘，在消控室可以直接手动控制喷淋泵的启动和停止。

4.5 水流指示器、信号阀、压力开关、喷淋消防泵的启动和停止的动作信号应反馈至消防联动控制器。

5、本工程火灾报警线缆室内敷设穿管采用套接紧定热镀锌钢管JDG，其壁厚不小于1.5mm，沿墙、顶板明敷，明敷管均需刷防火涂料保护。


6、其它未尽之处按有关国家规范执行。


[illegible]




注: 导线选择表(平面图中未标注导线如下)


信号总线	—————	NH-RVS-2x1.5 JDG20
信号+电源总线	—————	XY——NH-RVS-2x1.5+NH-BV-2x2.5 JDG25

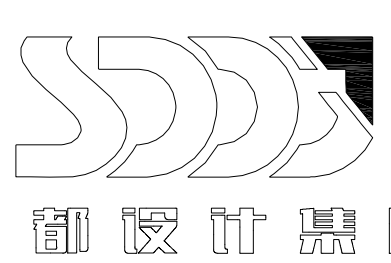日期 Date		版次 Ver.		版次说明 Description	
建设单位 Client 扬州江药业集团有限公司					
设计单位 Design Institute  SHENYOU DESIGN GROUP					
项目名称 Project Name					
子项目名称 Sub-Project					
项目编号 Project No.		姓名 Name		子项目编号 Sub-Project No.	
职 责 Responsibility		姓 名 Name		签 字 Signature	
审 定 Approved by		陆岳		陆岳	
设计负责人 Principal in Charge		黄震		黄震	
审 核 Checked by		马祥胜		马祥胜	
校 对 Verified by		董晓俊		董晓俊	
专业负责人 Specialized Responsible		马祥胜		马祥胜	
设 计 Designed by		唐忠荣		唐忠荣	
绘 图 Drawn by		唐忠荣		唐忠荣	
图纸名称 Sheet Title 一层火灾自动报警平面图					
专 业 Specialty		电 气		阶 段 Stage	
图 号 Sheet No.		电施-02		版 次 Ver.	
施工图 1					
执业签章 Registration Stamp					
出图签章 Release Stamp					
本图须加盖出图签章,否则一律无效 Issued Unless Stamped					

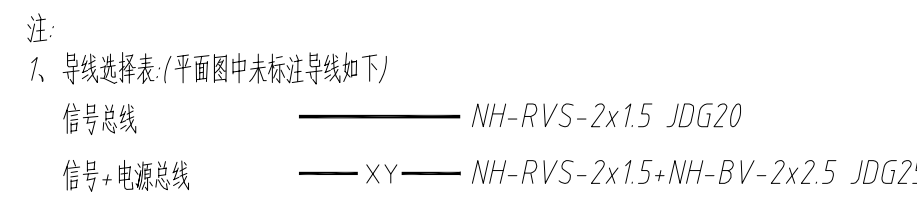


版次 Rev.		版次说明 Description	
建设单位 Client		扬子江药业集团有限公司	
设计单位 Design Institute		SHENDU DESIGN GROUP	
项目名称 Project Name		子项名称 Sub-Project	
子项编号 Project No.		子项编号 Sub-Project No.	
职 责 Responsibility		姓 名 Name	
审 定 Approved by		签 字 Signature	
审 核 Reviewed by		日 期 Date	
计 费 负 责 人 Principal in charge		陆 岳	
审 核 Checked by		黄 震	
校 对 Checked by		马祥胜	
专业负责人 Responsible		董晓俊	
设 计 Designed by		马祥胜	
绘 图 Drawn by		唐忠荣	
图纸名称 Sheet Title		唐忠荣	
二层火灾自动报警平面图			
专 业 Discipline		阶 段 Stage	
图 号 Sheet No.		施 工 图	
电气 - 03		版 次 Rev.	
注册盖章 Registration Stamp		1	
出图签章 Release Stamp			
本图须加盖出图签章, 否则一律无效 Unseal shall Stamp			



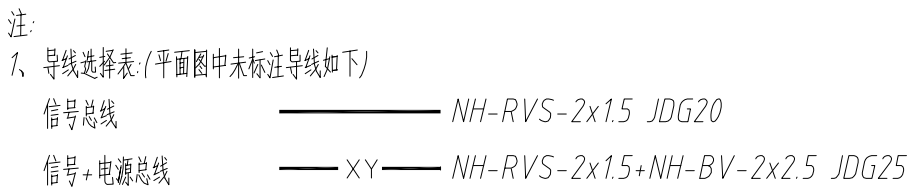



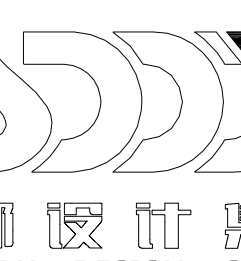
日期 Date		版次 Ver.		版次说明 Description	
建设单位 Client 扬州子江药业集团有限公司					
设计单位 Design Institute  SHENOU DESIGN GROUP					
项目名称 Project Name					
子项名称 Sub-Project					
项目编号 Project No.		姓 名 Name		子项编号 Sub-Project No.	
职 责 Responsibility		姓 名 Name		签 字 Signatures	
审 定 Approved by		陆 岳		陆 岳	
设计负责人 Principal in charge		黄震		黄震	
审 核 Reviewed by		马祥胜		马祥胜	
校 对 Checked by		董晓俊		董晓俊	
专业负责人 Responsible		马祥胜		马祥胜	
设 计 Designed by		唐忠荣		唐忠荣	
绘 图 Drawn by		唐忠荣		唐忠荣	
图纸名称 Sheet Title 三层火灾自动报警平面图					
专 业 Discipline		电 气		阶 段 Stage	
图 号 Sheet No.		电施-04		版 次 Ver.	
施工图 7					
执业签章 Registration Stamp					
出图签章 Release Stamp					
本图须加盖出图签章,否则一律无效 Enroll Release Stamp					

会议	建筑	给排水	强电	景观	动力
会	结构	暖通	弱电	室内	人防
经	确认 by				人防工程

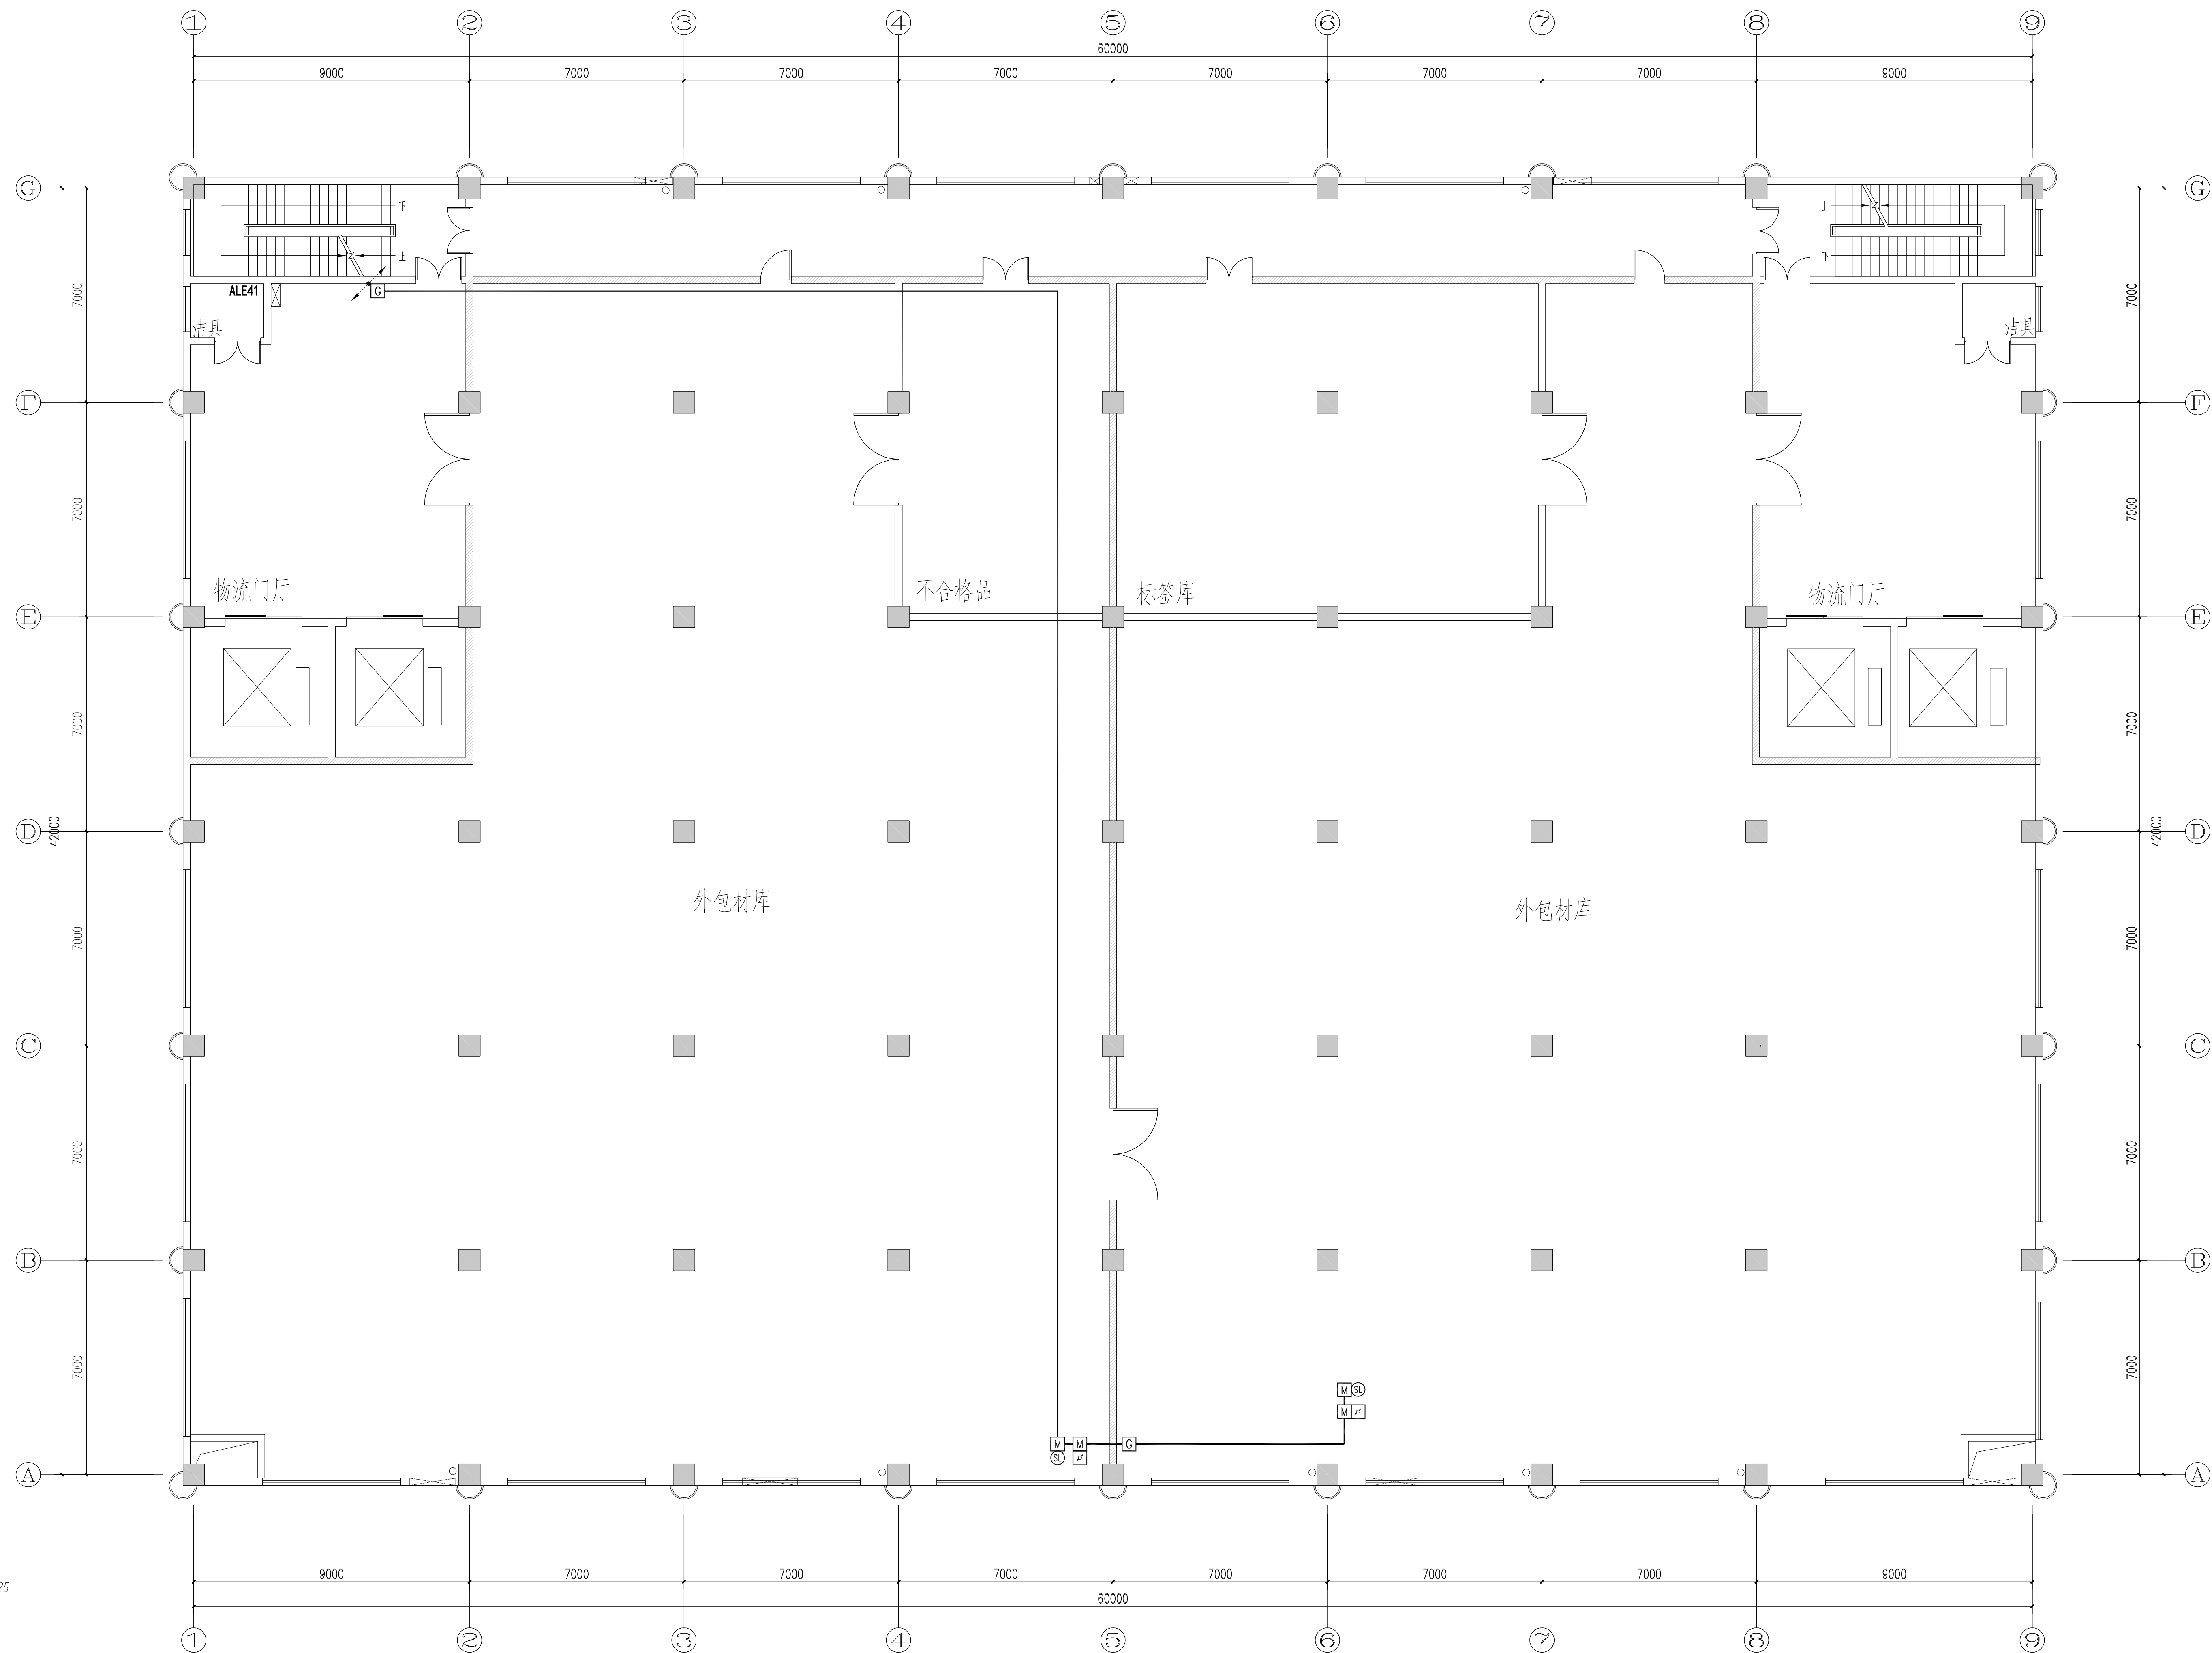


四层火灾自动报警平面图

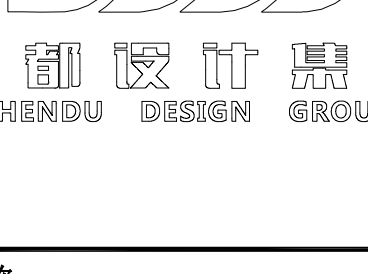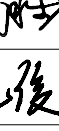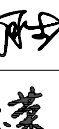日期 Date	版次 Ver.	版次说明 Description	
建设单位 Client			
扬子江药业集团有限公司			
设计单位 Design Institute			
			
项目名称 Project Name			
子项名称 Sub-Project			
项目编号 Project No.		子项编号 Sub-Project No.	
职 责 Responsibility	姓 名 Name	签 字 Signature	日 期 Date
审 定 Approved by	陆岳 黄震	陈云  马祥胜	
设计负责人 Principal in charge	马祥胜		
核 核 Reviewed by	董晓俊		
校 对 Checked by	马祥胜		
专业负责人 Professional Responsibility	唐忠荣		
设 计 Designed by	唐忠荣		
绘 图 Drawn by	唐忠荣		
图纸名称 Sheet Title			
四层火灾自动报警平面图			
专 业 Majority	电 气	阶 段 Stage	施工图
图 号 Sheet No.	电施-05	版 次 Ver.	1
执业签章 Registration Stamp			
出图签章 Release Stamp			
本图须加盖出图签章，否则一律无效 Issued Unless Stamped			

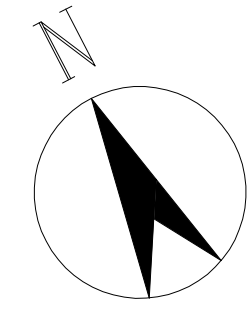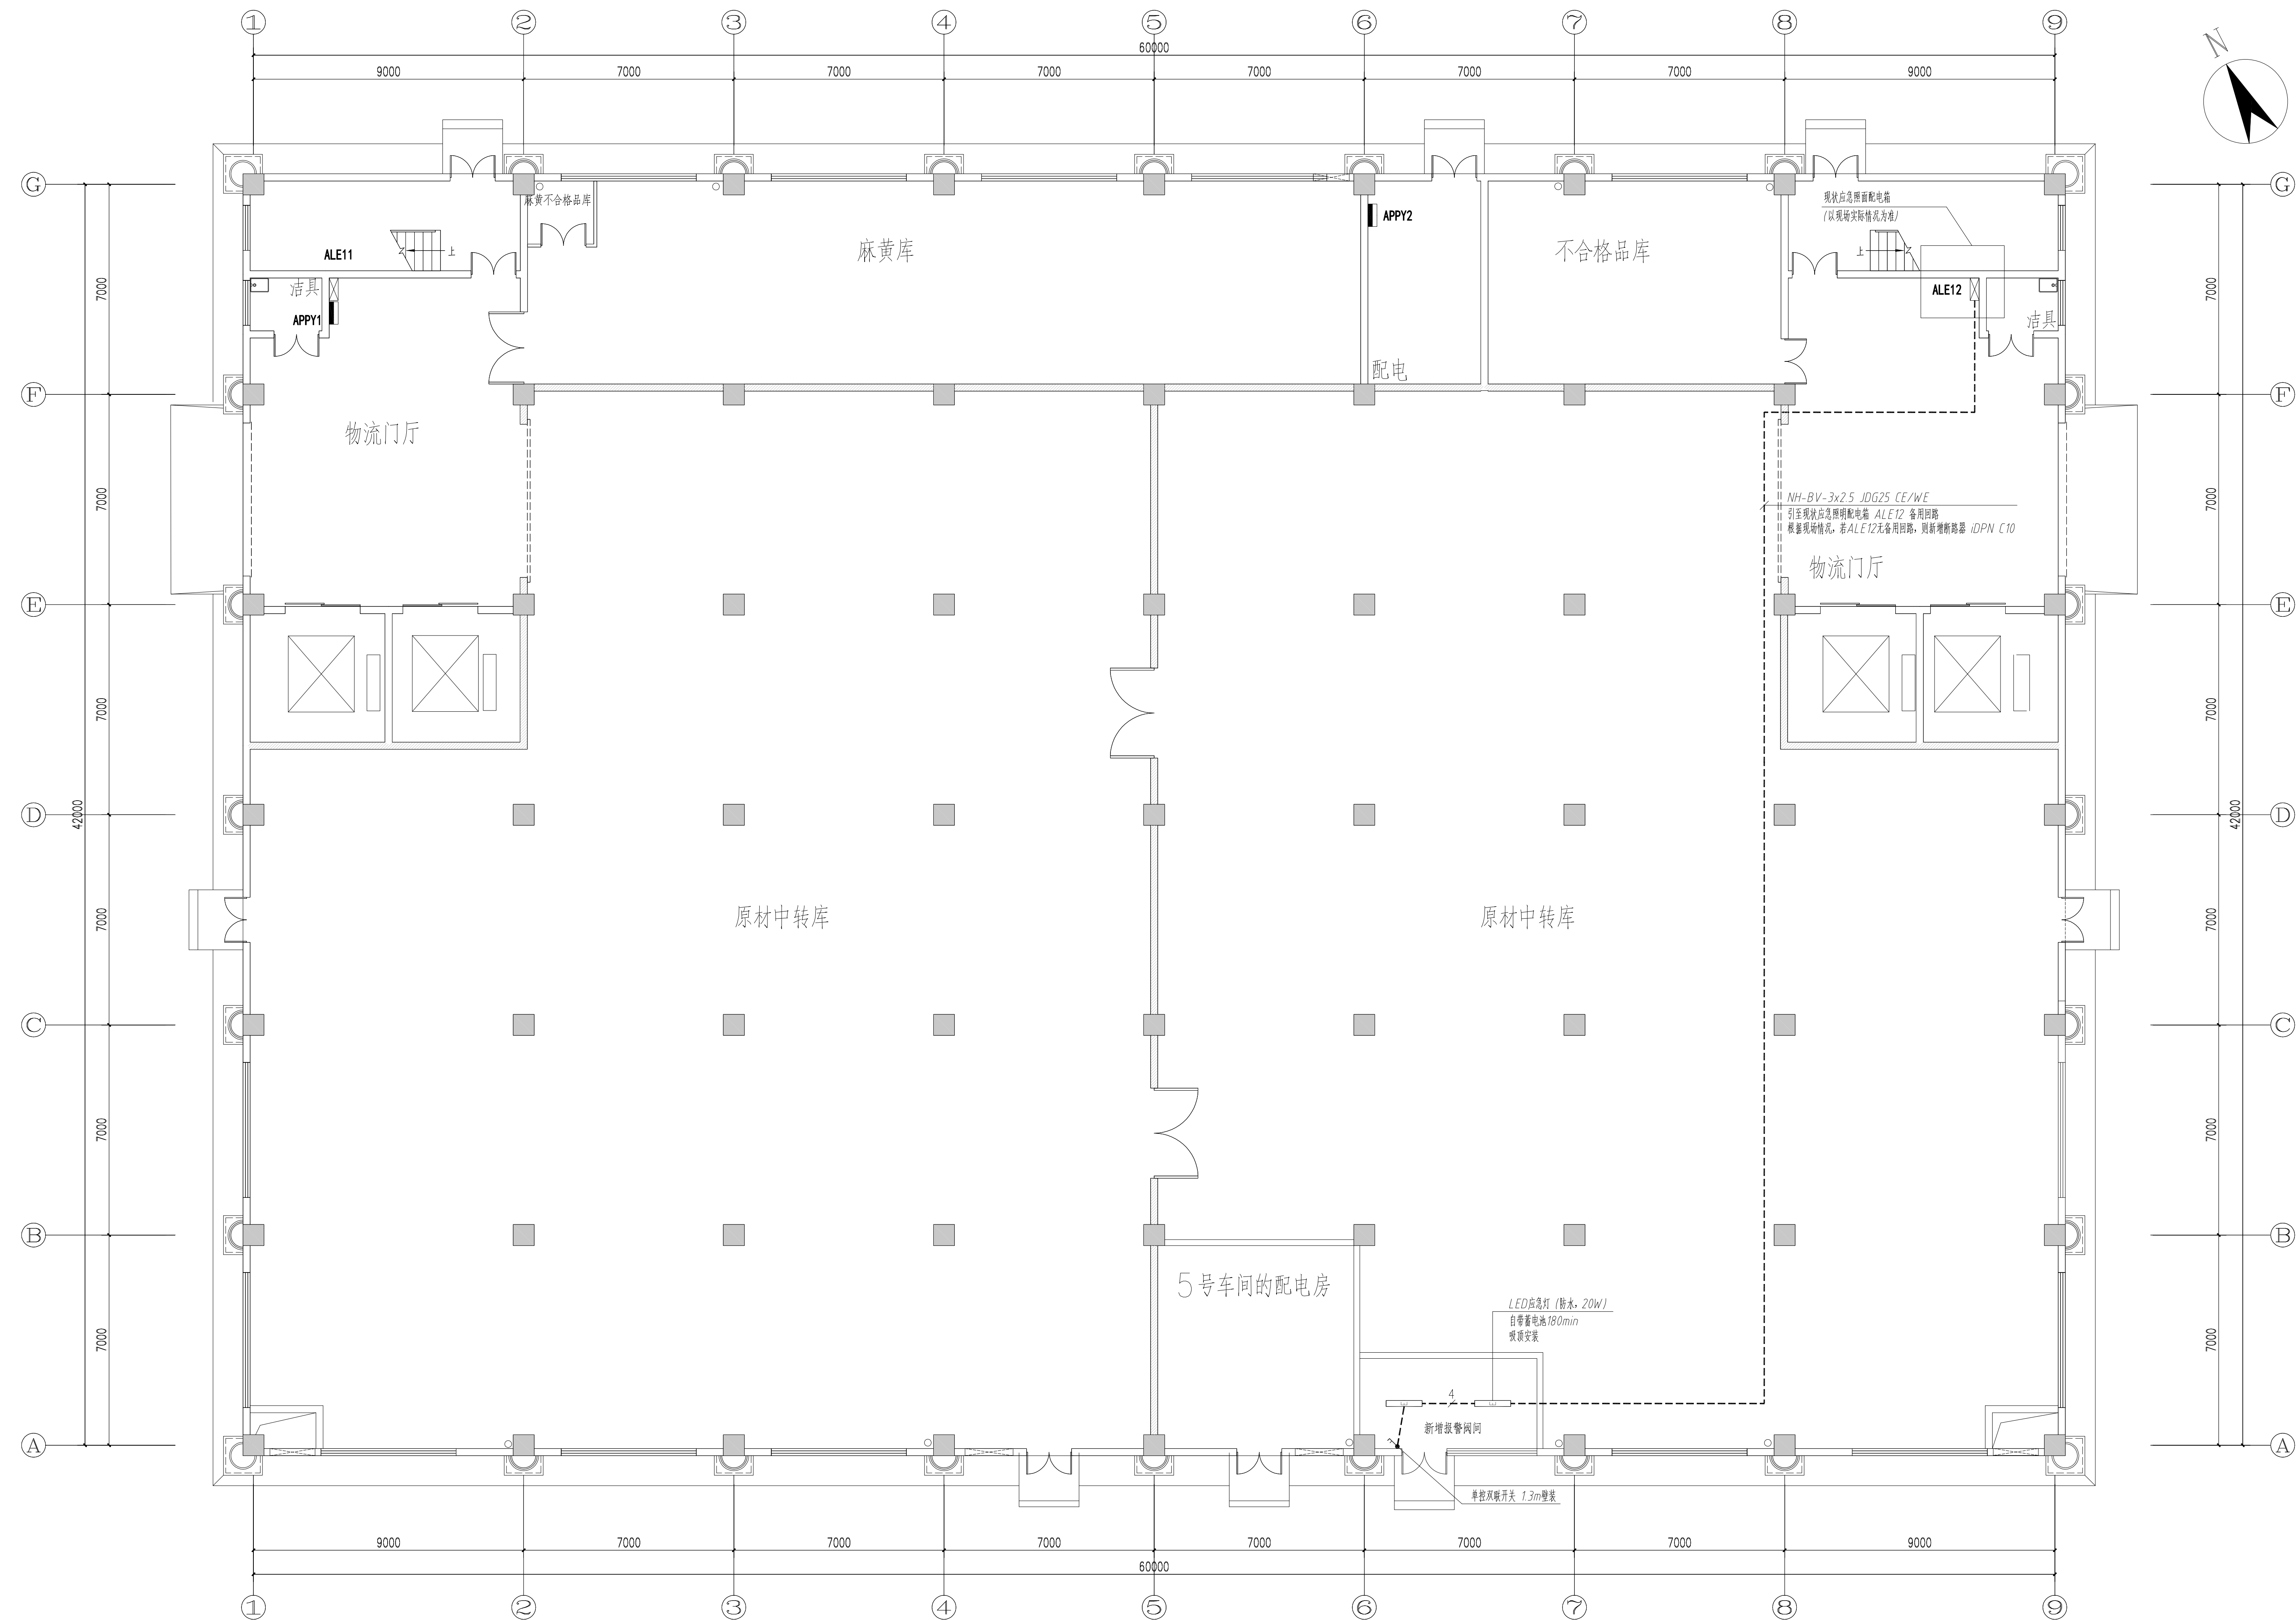

会 员 建 筑	给 排 水	强 电	暖 通	照 明	消 防	特 殊 功 能	其 他	备 注
会 员 建 筑	给 排 水	强 电	暖 通	照 明	消 防	特 殊 功 能	其 他	备 注

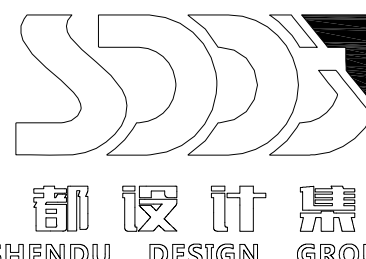日期 Date	版次 Rev.	版次说明 Description
建设单位 Client		
扬子江药业集团有限公司		
设计单位 Design Institute		
		
项目名称 Project Name		
子项名称 Sub-Project		
项目编号 Project No.		子项目编号 Sub-Project No.
职责 Responsibility	姓名 Name	签字 Signature
审 定 Approved by	陆岳	陆岳
设计负责人 Principal in charge	黄震	黄震
审 核 Reviewed by	马祥胜	马祥胜
校 对 Checked by	董晓俊	董晓俊
专业负责人 Specialized Responsible	马祥胜	马祥胜
设 计 Designed by	唐忠荣	唐忠荣
绘 图 Drawn by	唐忠荣	唐忠荣
图纸名称 Sheet Title		
一层照明平面图		
专 业 Discipline	电气	阶 段 Stage
图 号 Sheet No.	电施-06	施 工 图
执业签章 Registration Stamp		
出图印章 Release Stamp		
本图须加盖出图签章，否则一律无效 Unlaid Release Stamp		